


Protyasha Saba

# Architecture Portfolio

Department of Architecture  
Khulna University of Engineering & Technology

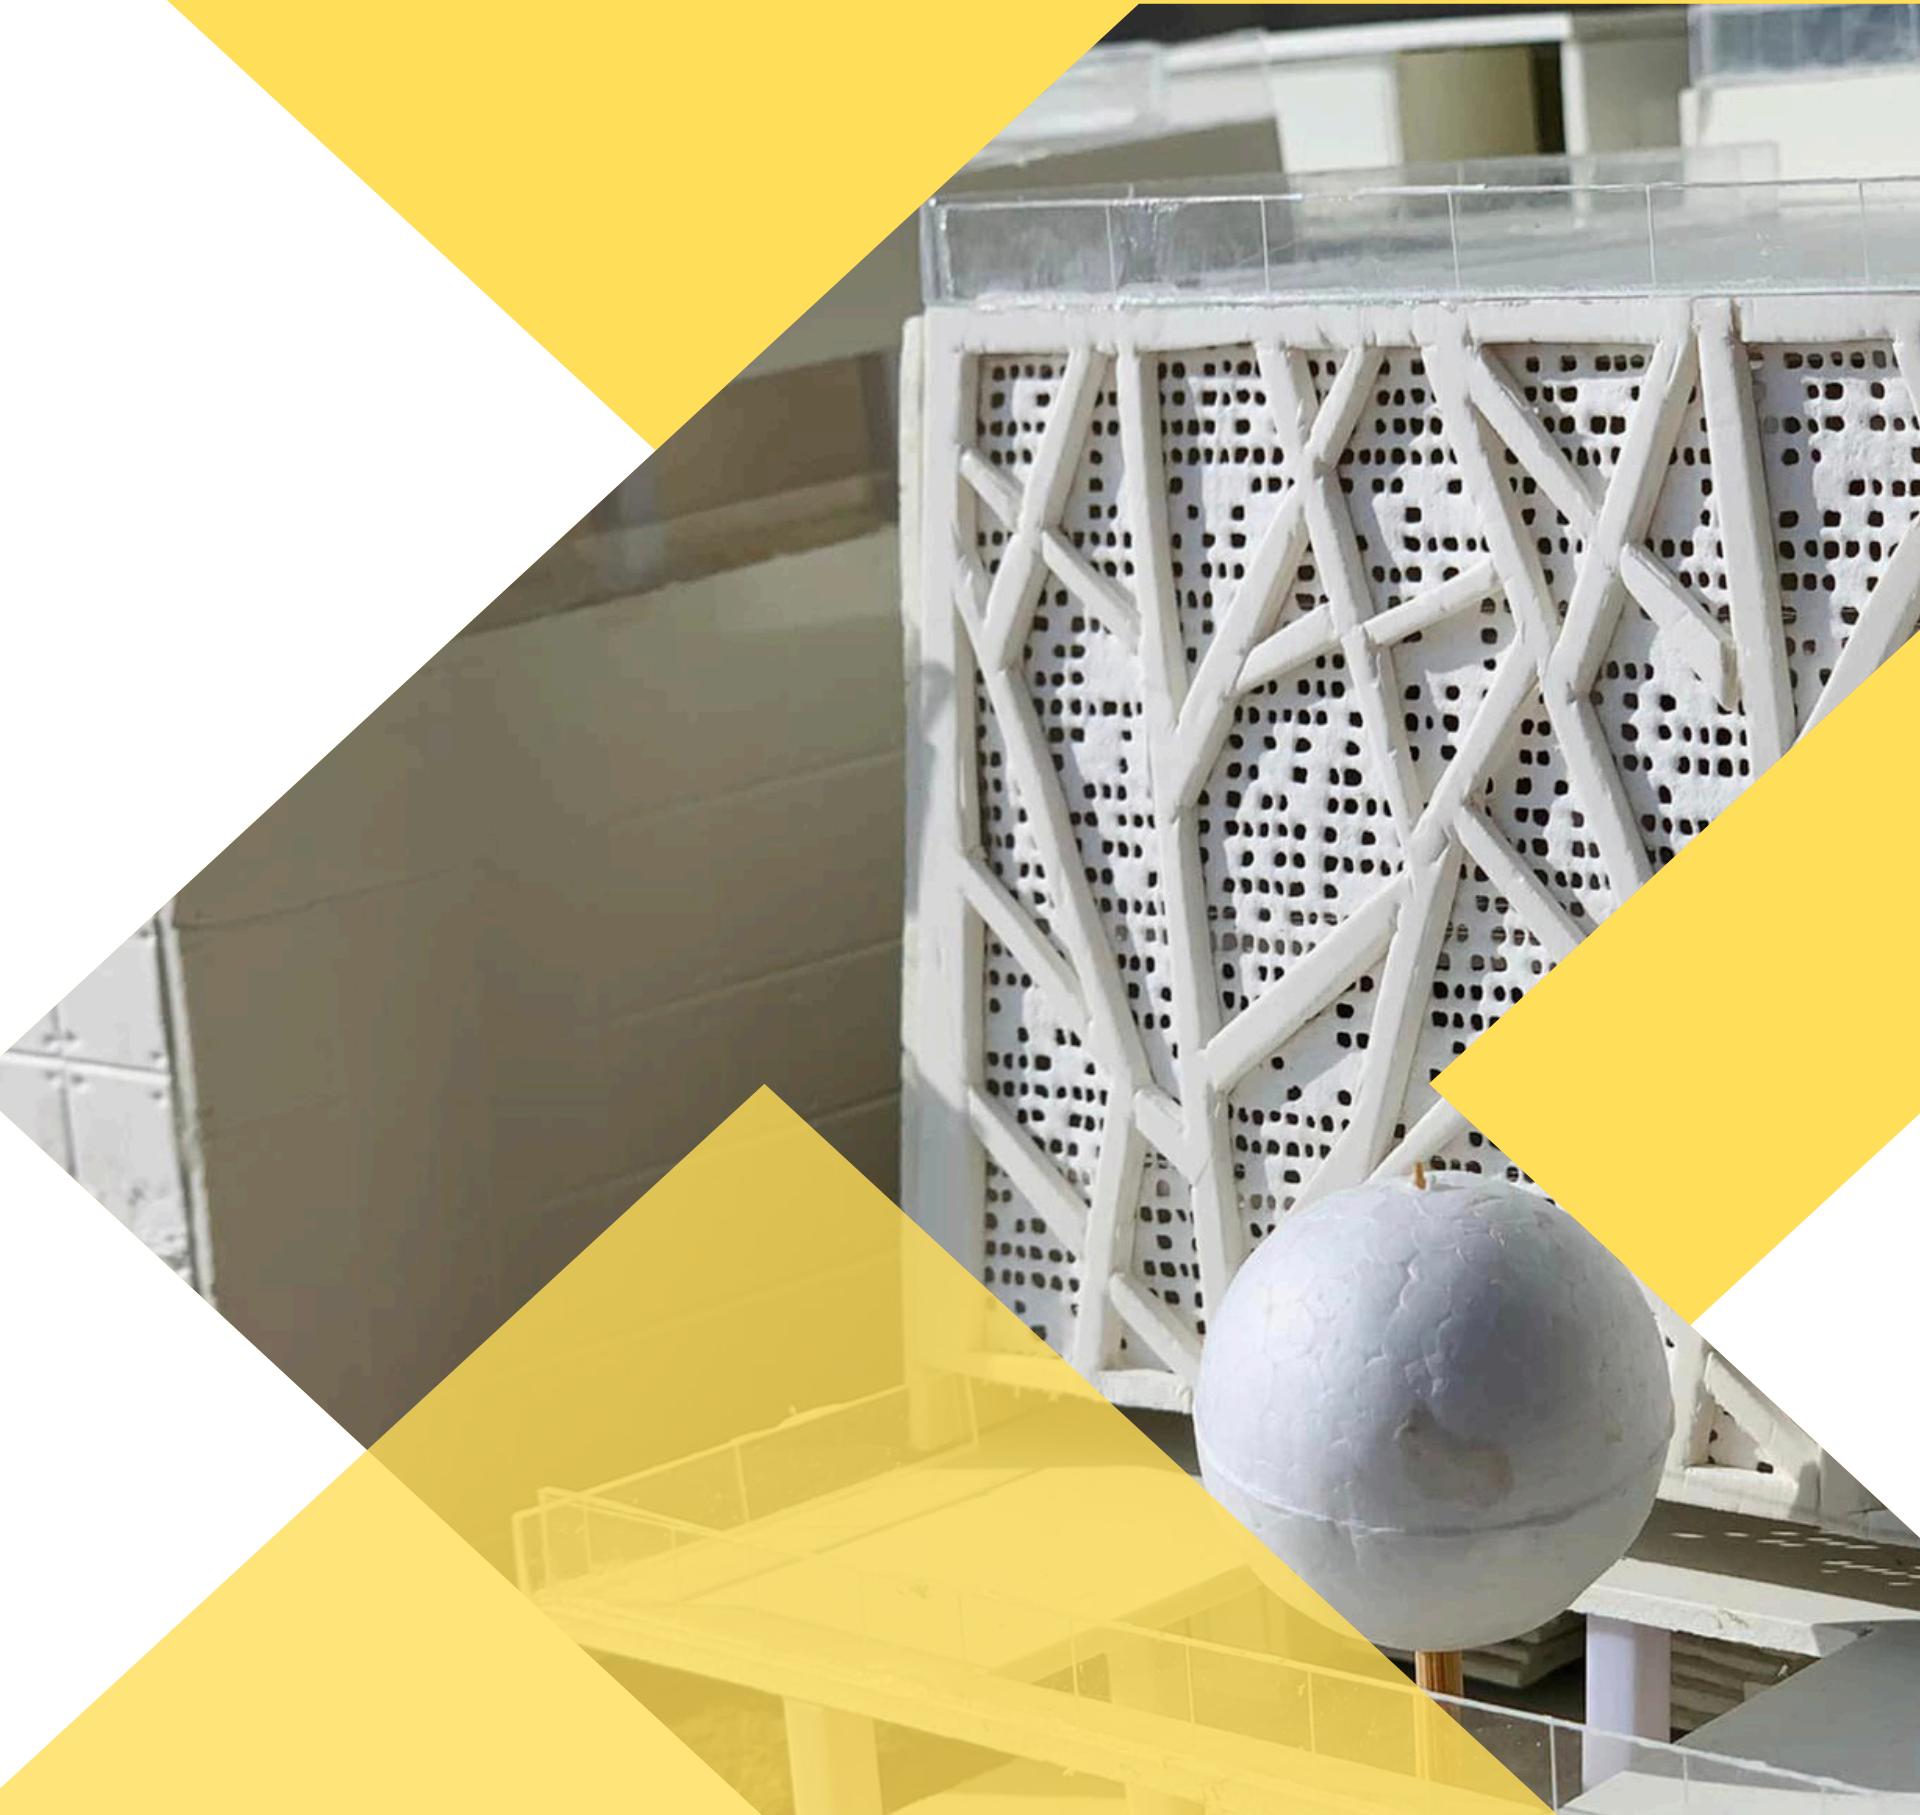

# Resume

## Protasha Saba

Fourth year, Department of Architecture,  
Khulna University of Engineering & Technology,  
Khulna

+8801713424407  
saba1925019@stud.kuet.ac.bd  
Dhaka, Bangladesh


**Objective:** To learn about architecture and its practical aspects



## My Skills

AUTOCAD	● ● ● ● ●
SKETCHUP	● ● ● ● ●
PHOTOSHOP	● ● ● ● ●
POWERPOINT	● ● ● ● ●
LUMION	LEARNING

## What I like

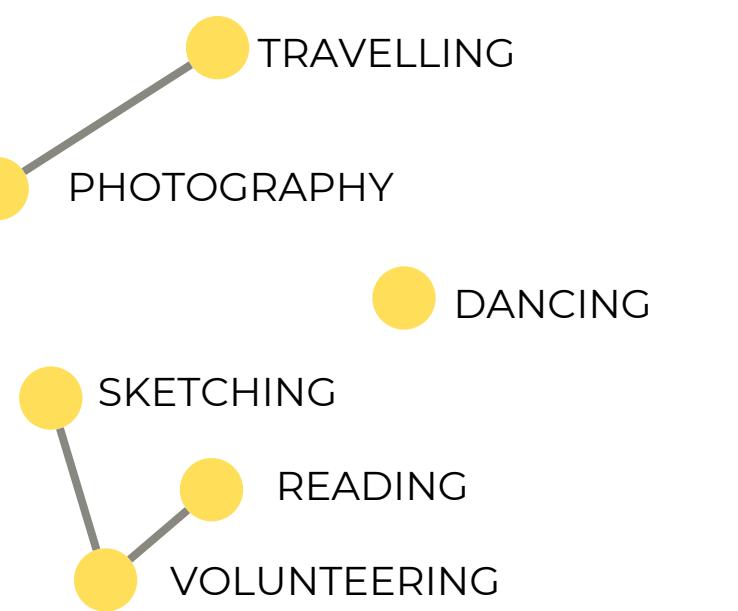

# Contents

- 
- 
- 1** A Studio Apartment For Professionals
  - 2** Community Women's Empowerment Center
  - 3** Vacation House: Living With Serenity
  - 4** Design of a Civic Center
  - 5** Embracing the Sky: Design of a Skyscraper

# A Studio Apartment For Professionals

Designing For A Chef



# A Studio Apartment For Professionals

Designing For A Chef

DESIGN STUDIO III



# **Community Women's Empowerment Center**

Designing In The Masters' Footsteps (Geoffrey Bawa)



# **Community Women's Empowerment Center**

Designing In The Masters'  
Footsteps (Geoffrey Bawa)

DESIGN STUDIO IV



# Drafting

**COMMUNITY WOMEN'S EMPOWERMENT CENTER**  
DESIGNING IN THE MASTER'S FOOTSTEPS  
SCALE - 1:100  
STUDENT ID - 1925019

**CLOSER LOOK** This is the basic scheme made & exhibited at Major Award Building & Design. The project focus on the classic architecture and is designed by keeping the work done of Stanley Poon based on classic expressionism pillar material and colors.

**FORM DEVELOPMENT**

**ZONING**

Legend:  
■ AREAS  
□ CLASS ROOMS  
▨ KITCHEN

**GROUND FLOOR PLAN AT 3150mm**

**FIRST FLOOR PLAN AT 6300mm**

**SECOND FLOOR PLAN AT 7950mm**

**TOP VIEW**

**EAST ELEVATION**

**NORTH ELEVATION**

**WEST ELEVATION**

**SOUTH ELEVATION**

**SECTION AA'**

**SECTION BB'**

# Vacation House

Living In Serenity


DESIGN STUDIO IV




# Vacation House

Living In Serenity

DESIGN STUDIO IV

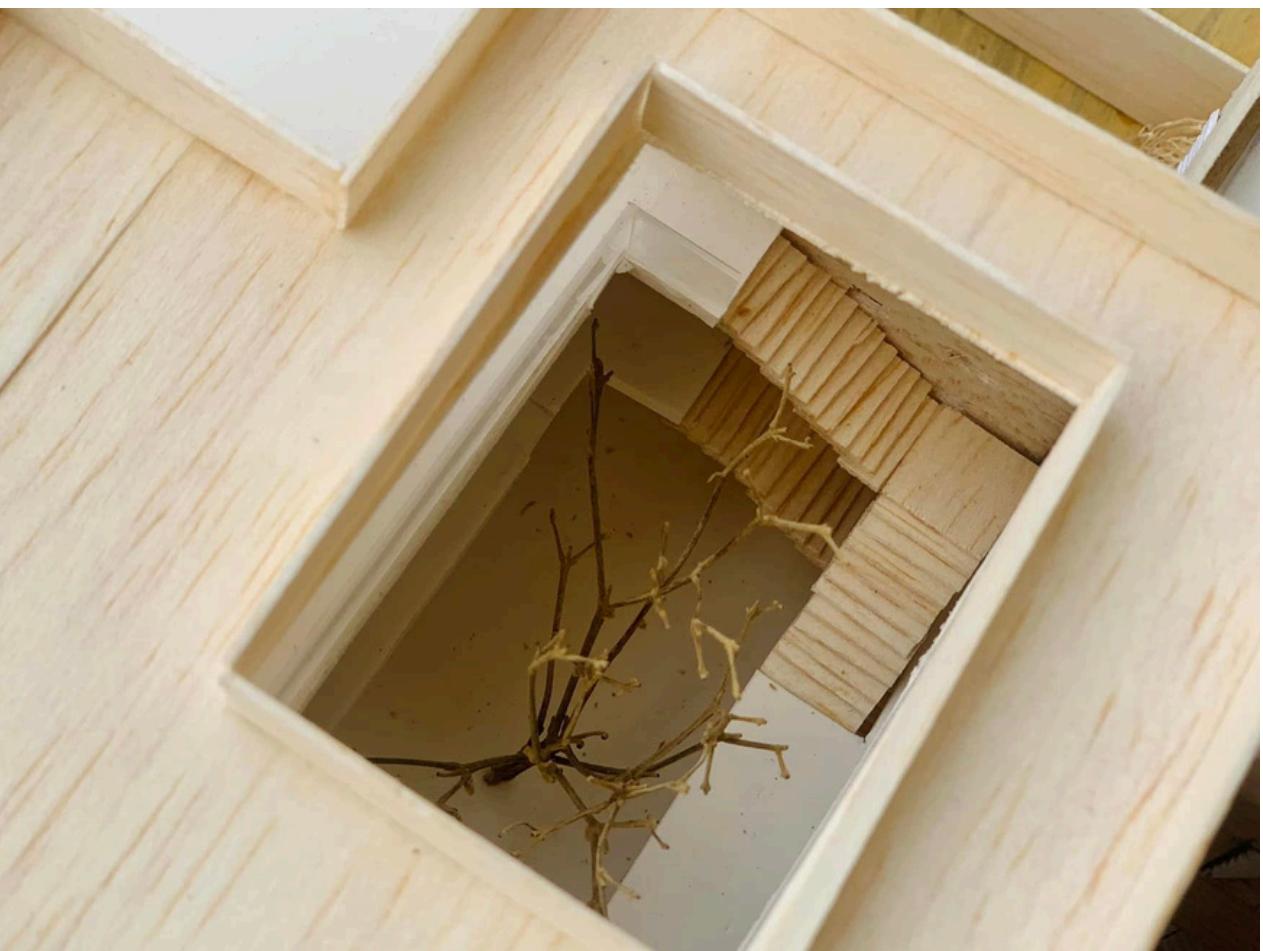

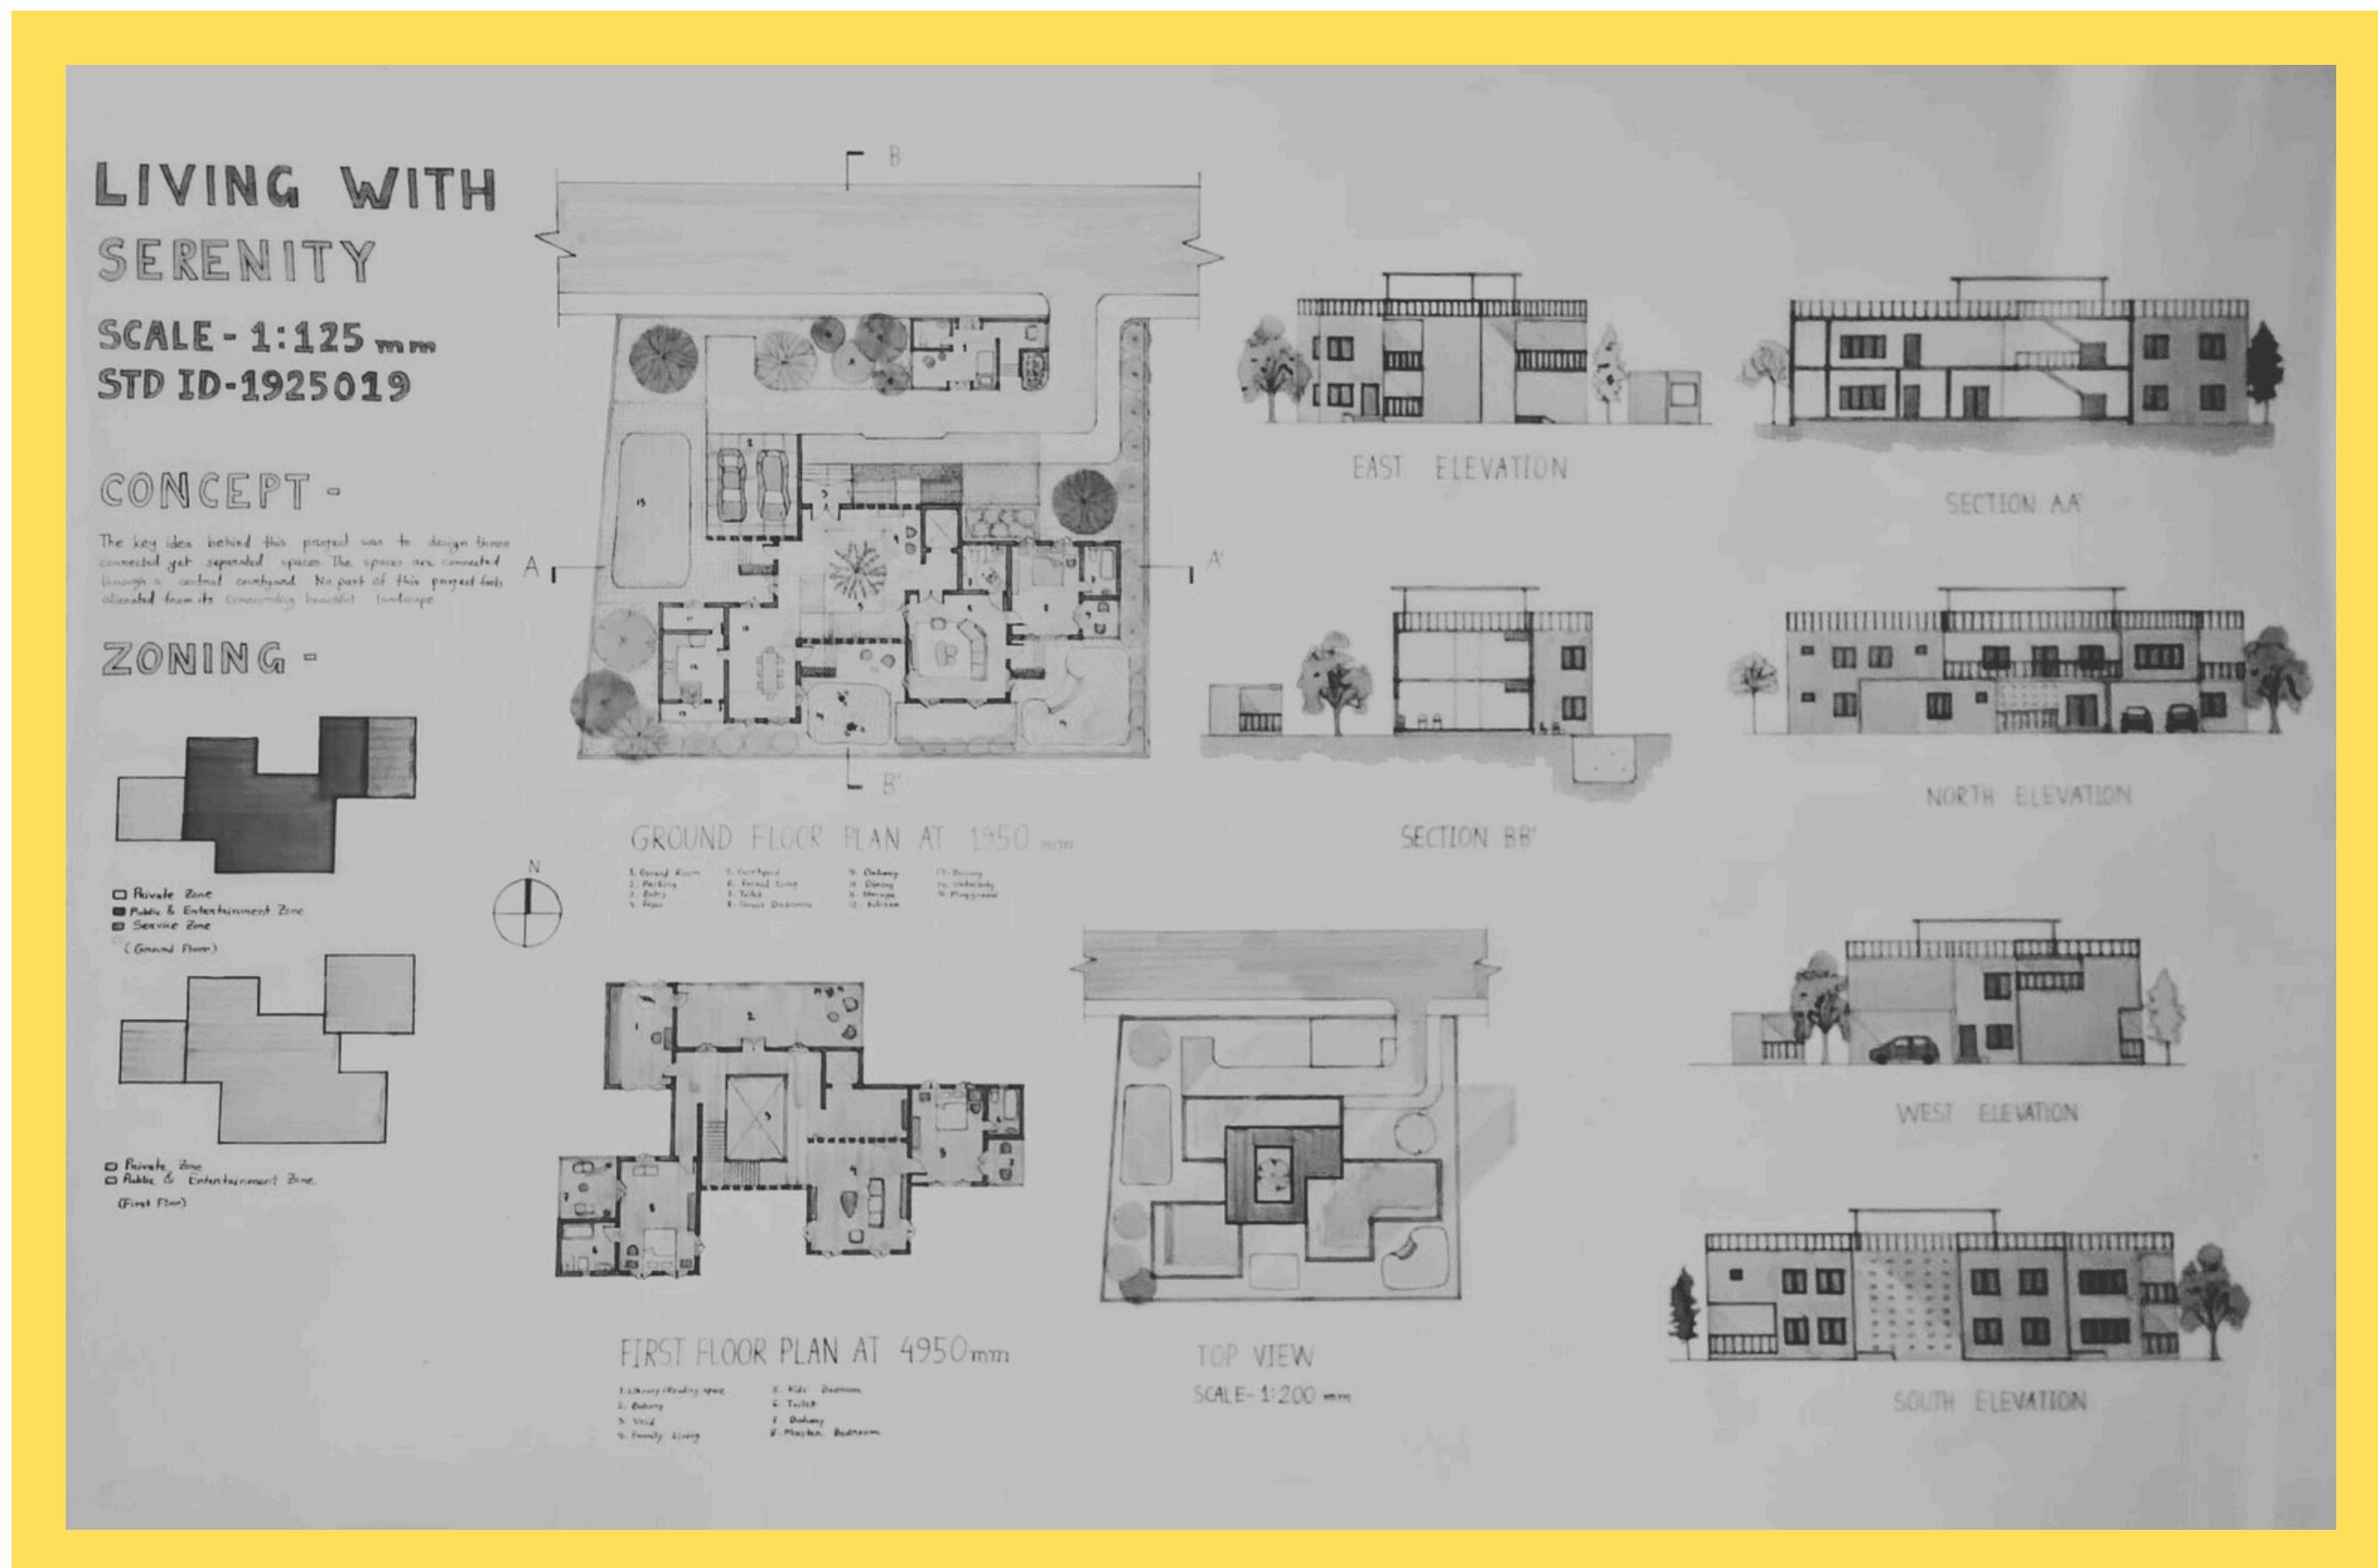




## **Design of a Civic Center**

Creating a ceremonial  
gathering space that  
welcomes everyday use





# Design of a Civic Center

Creating a ceremonial gathering space that welcomes everyday use

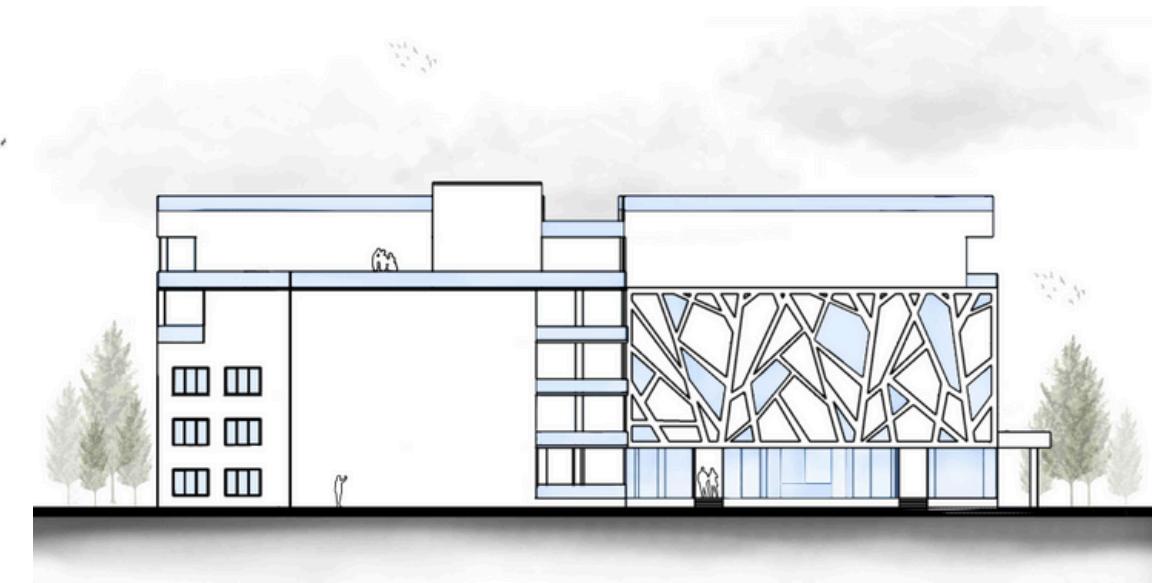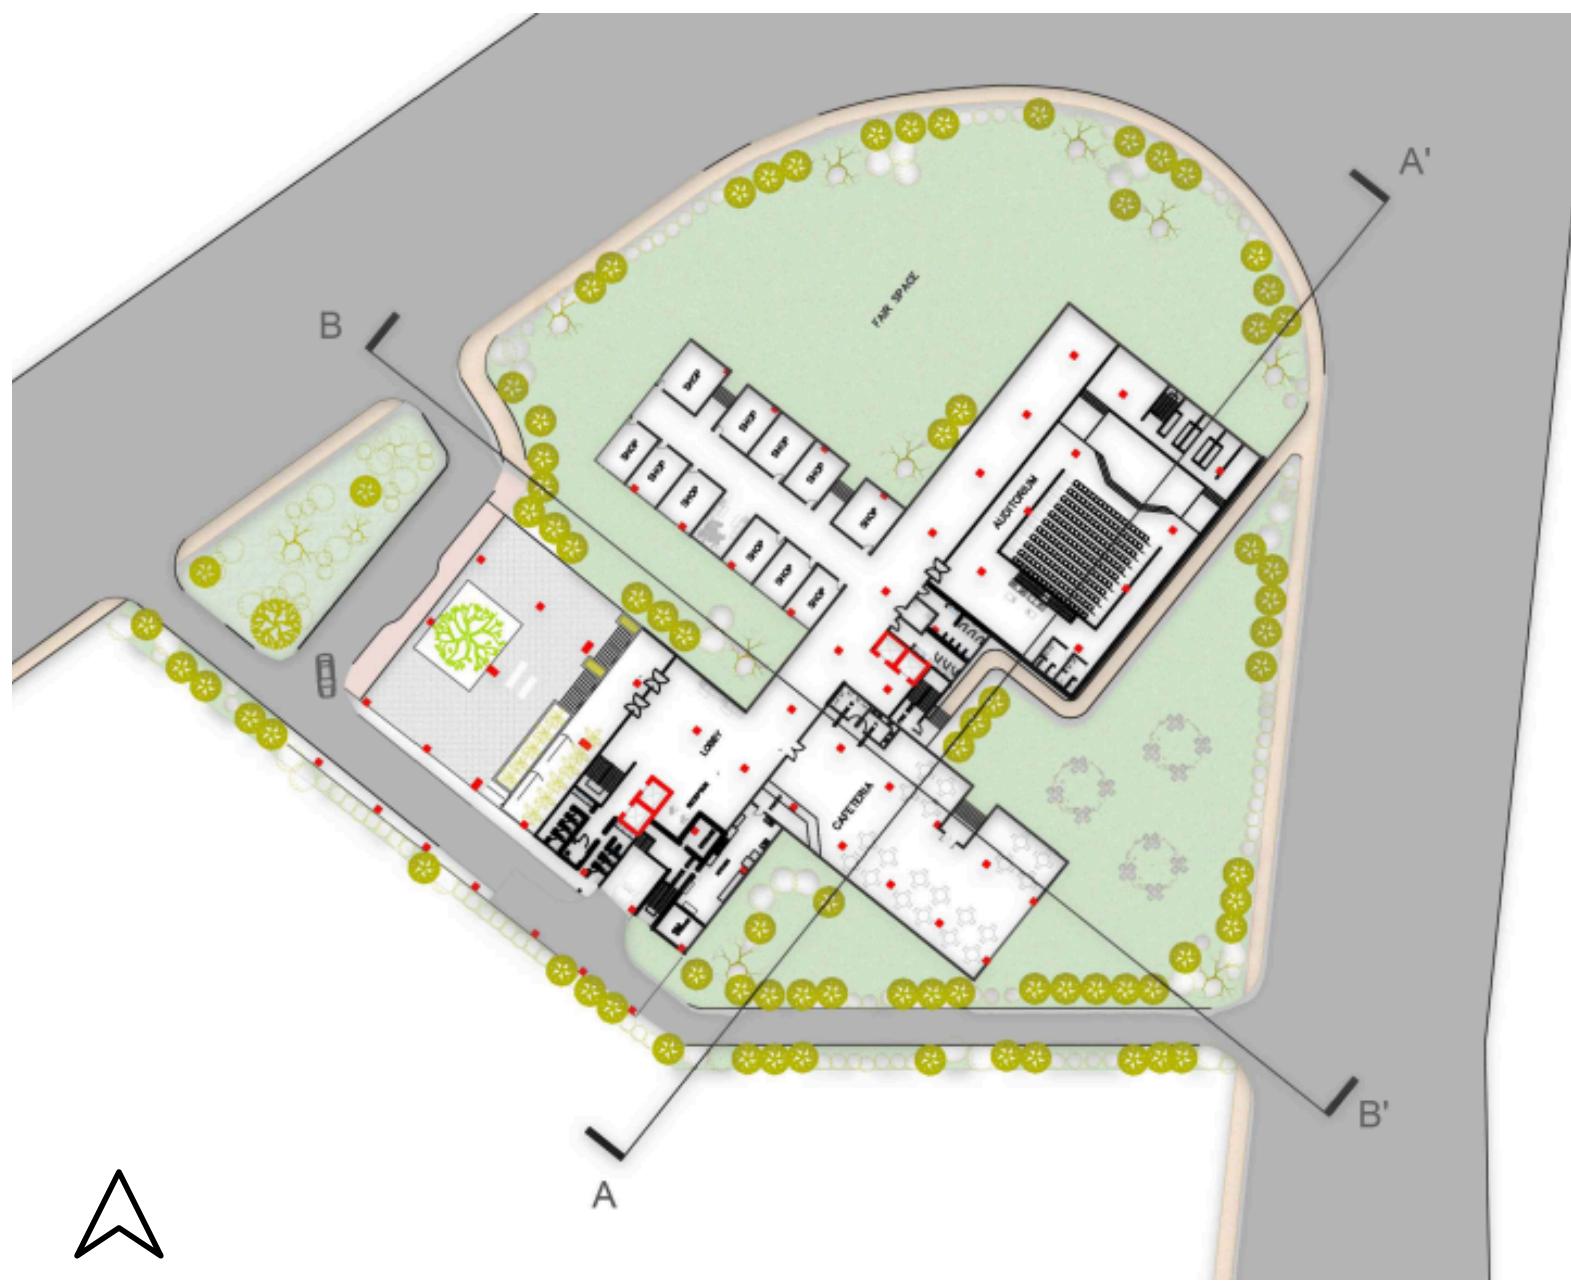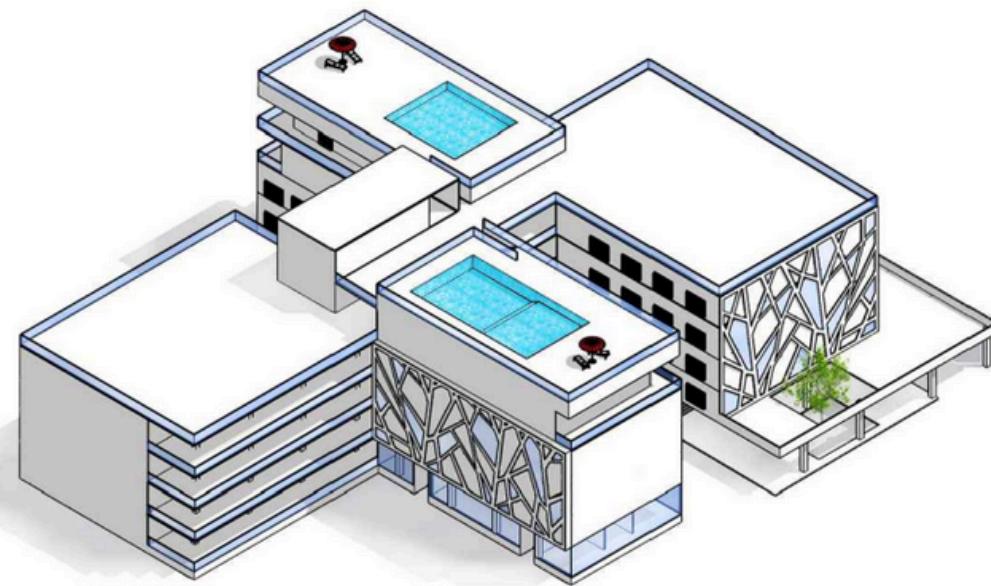




# Embracing the Sky

Design of a Skyscraper

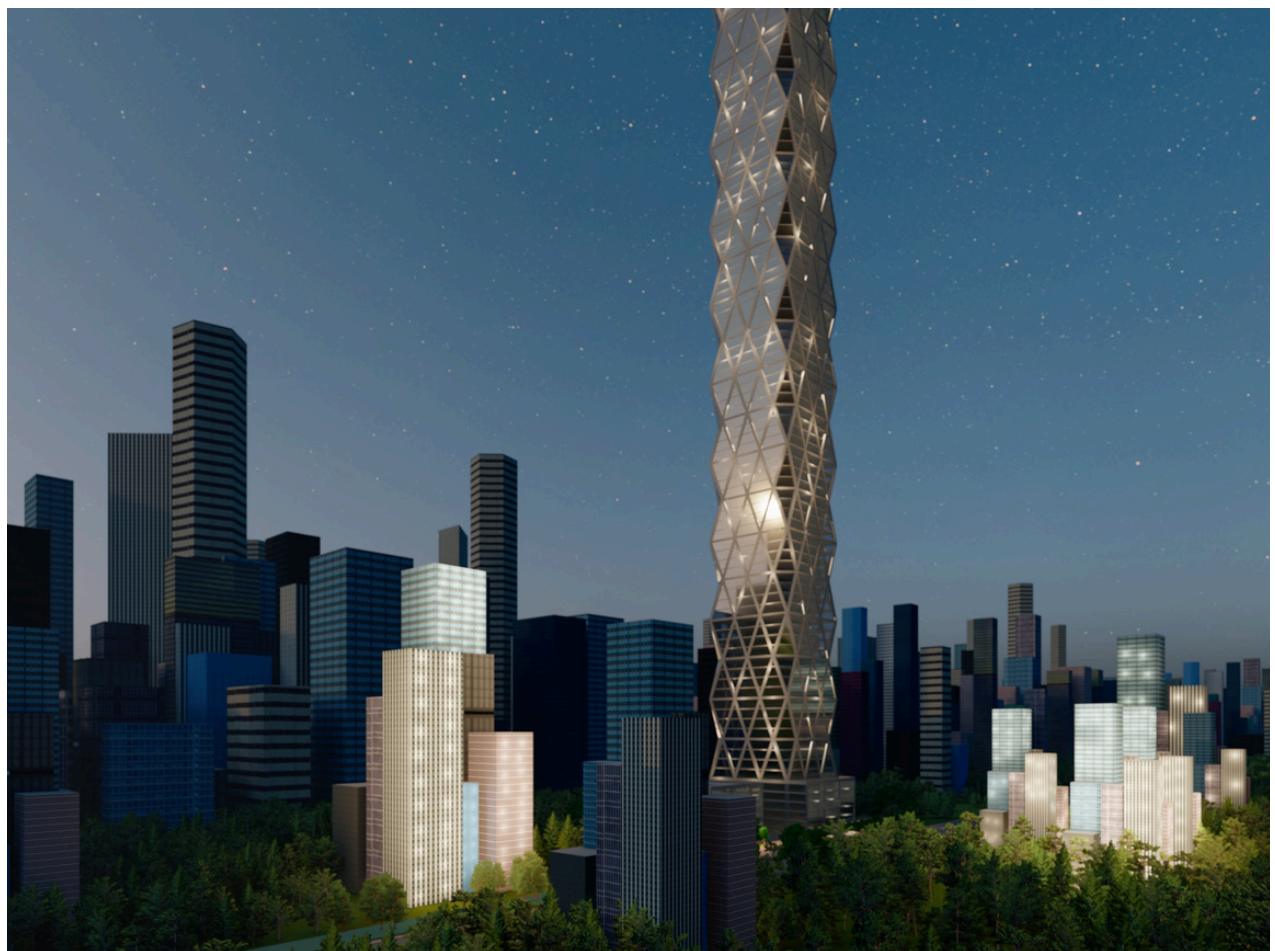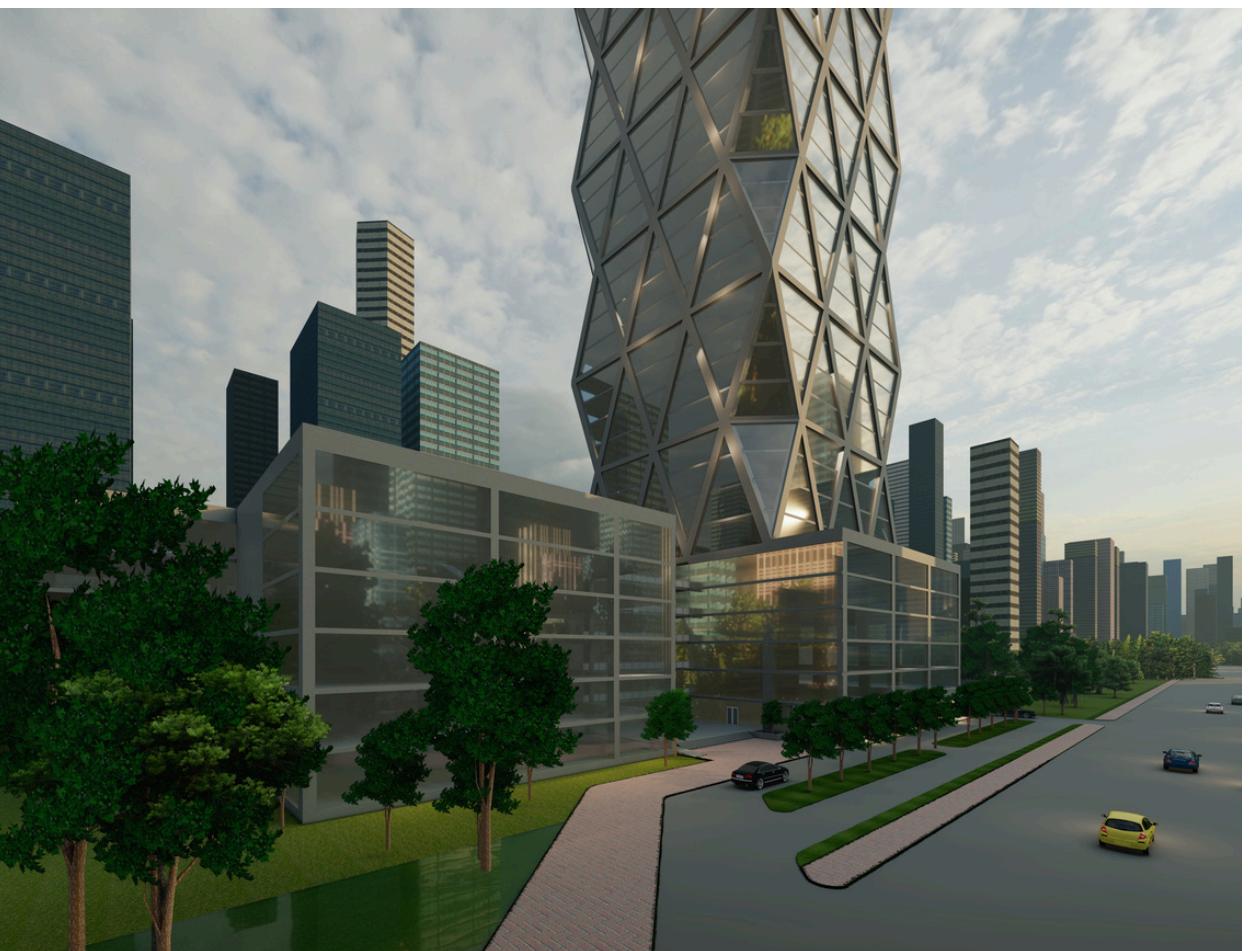

# Embracing the Sky: Design of a Skyscraper

Creating a new office highrise building typology by combining a public space with the private space; with a vision of creating a landmark.



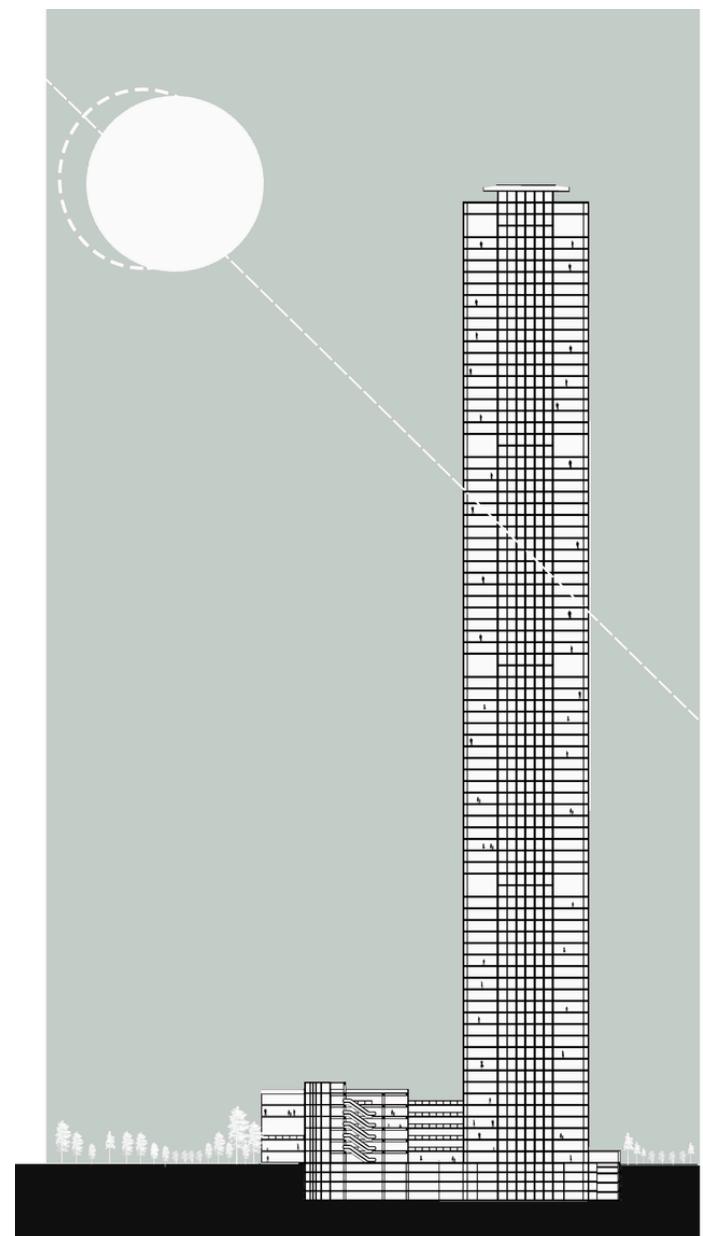
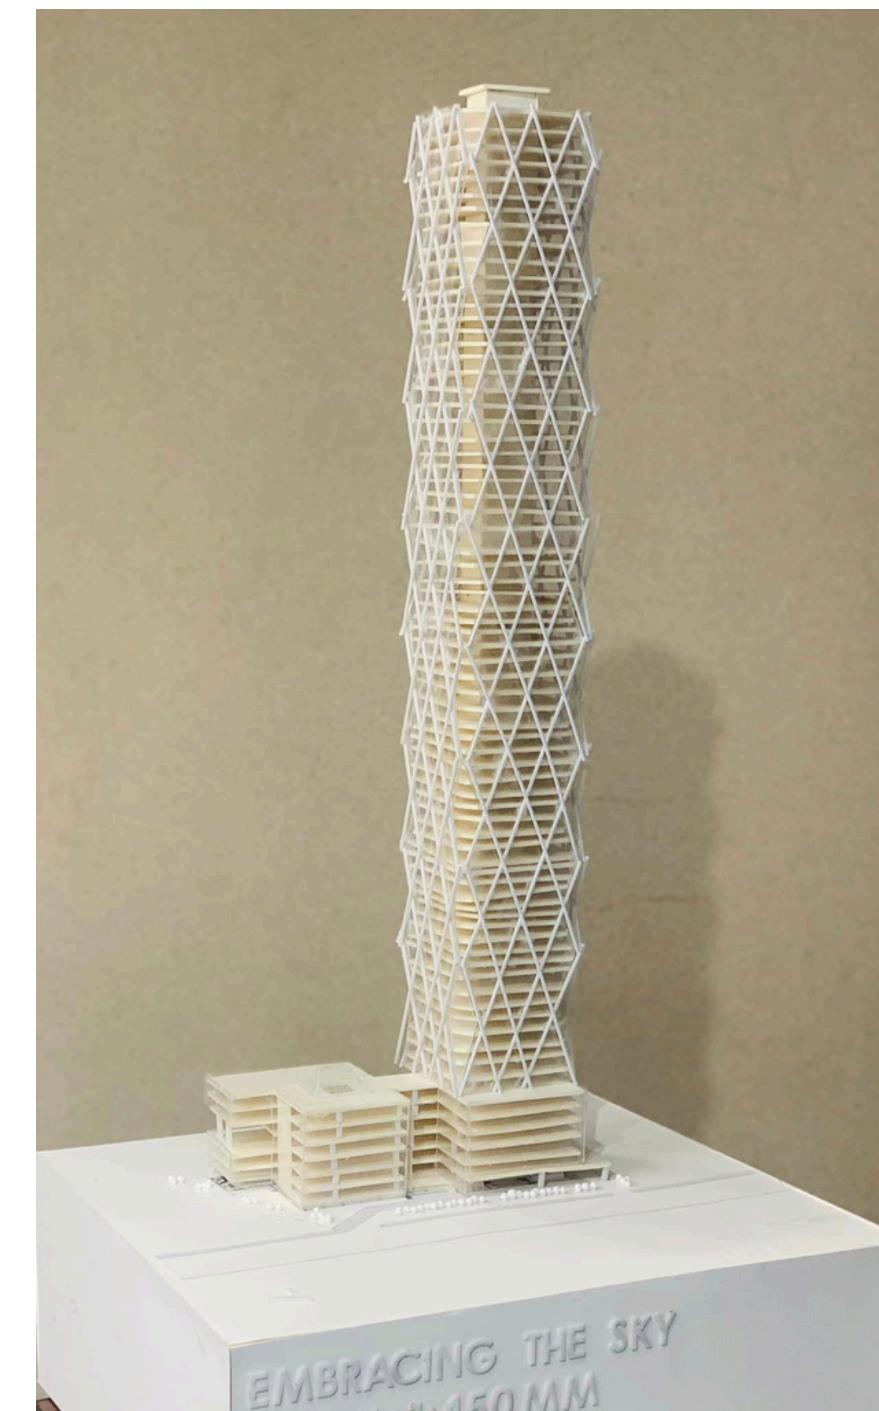
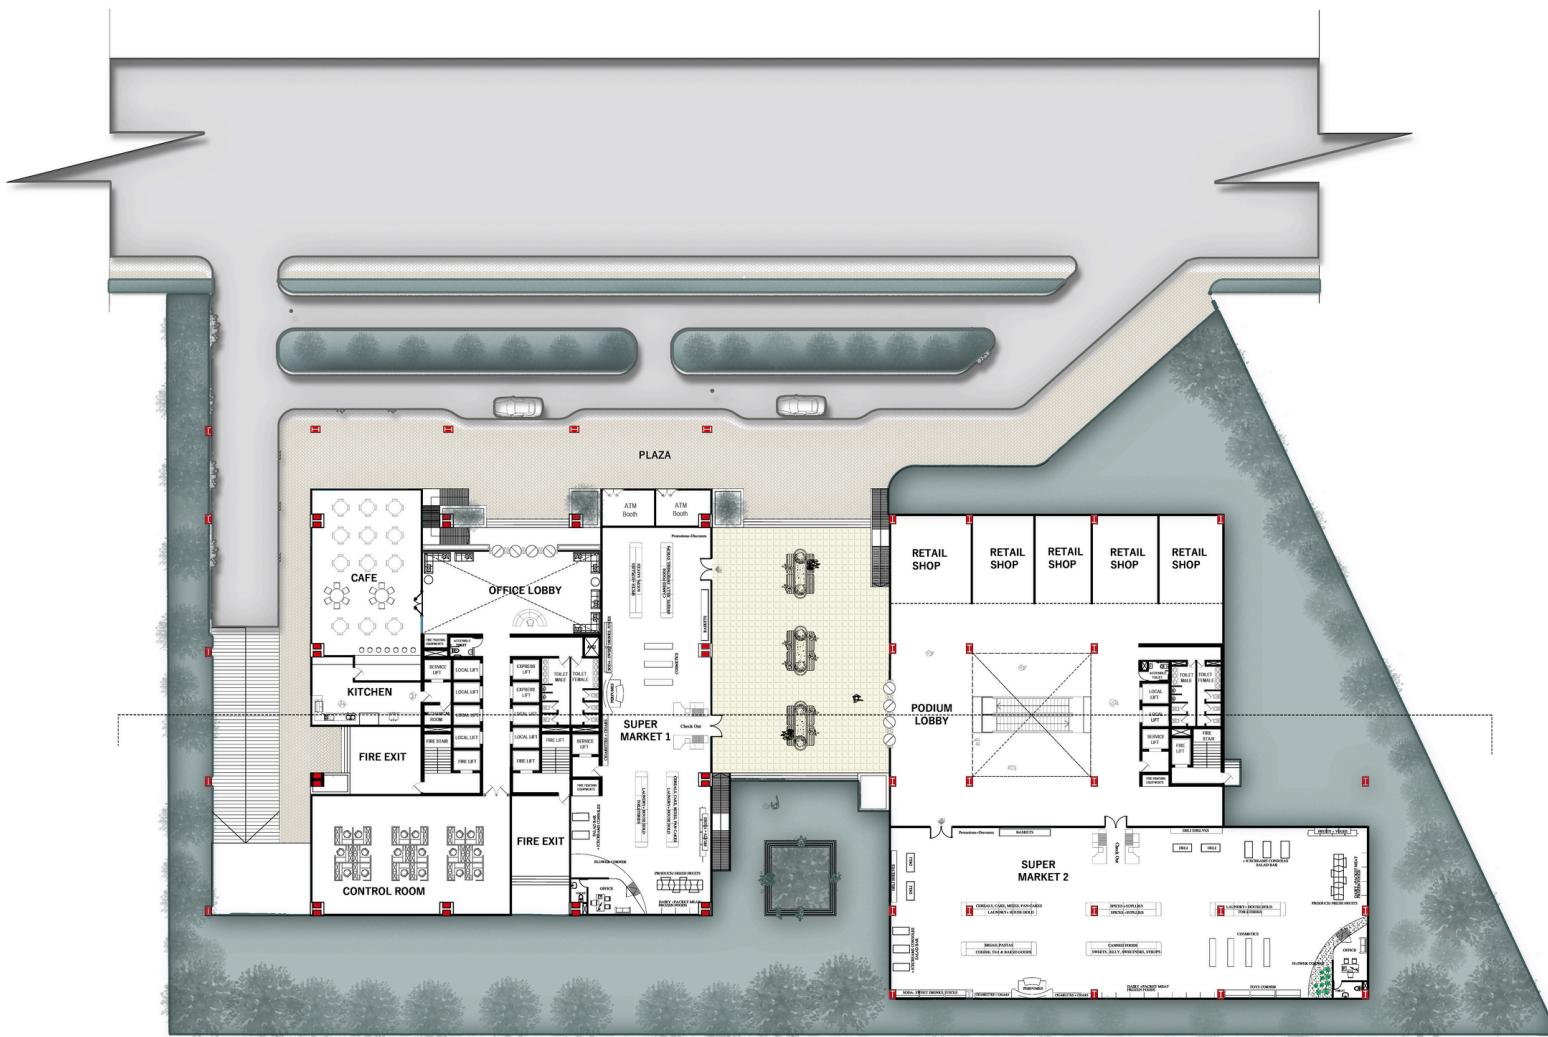


# Poster Design






Sculpting

# Sketching

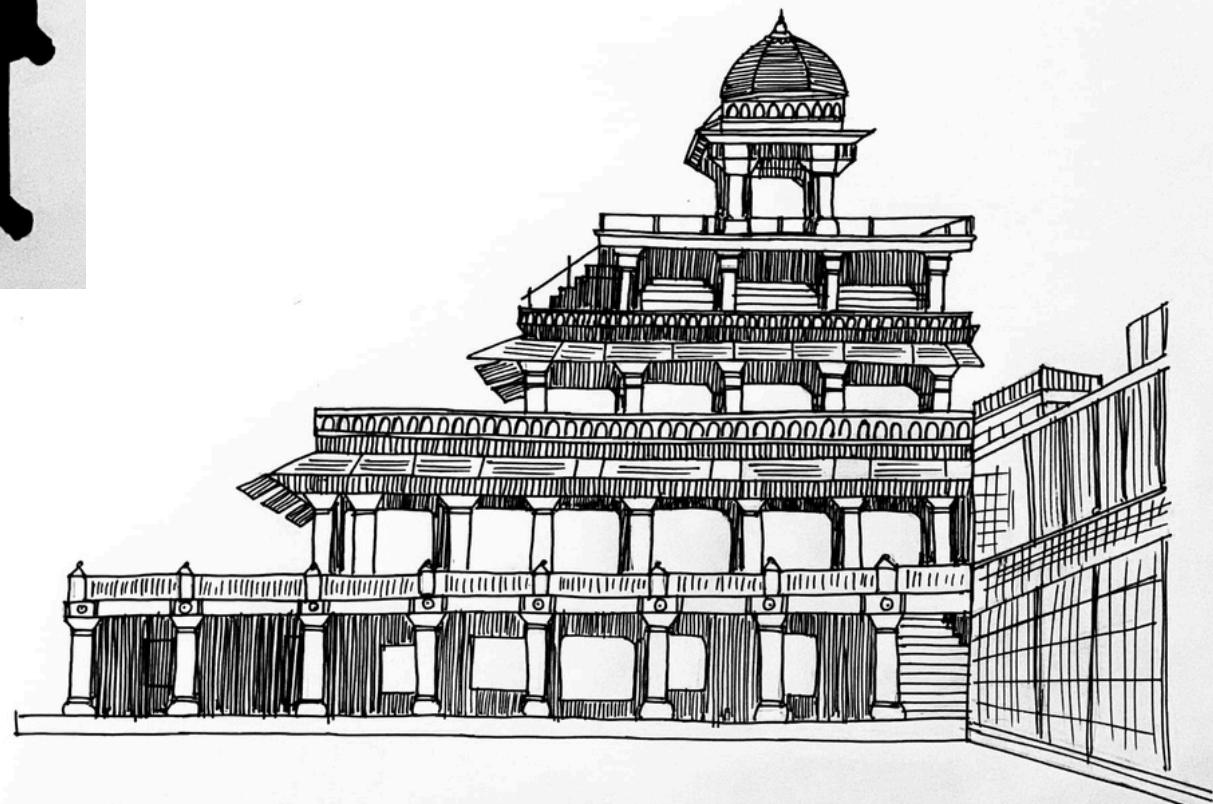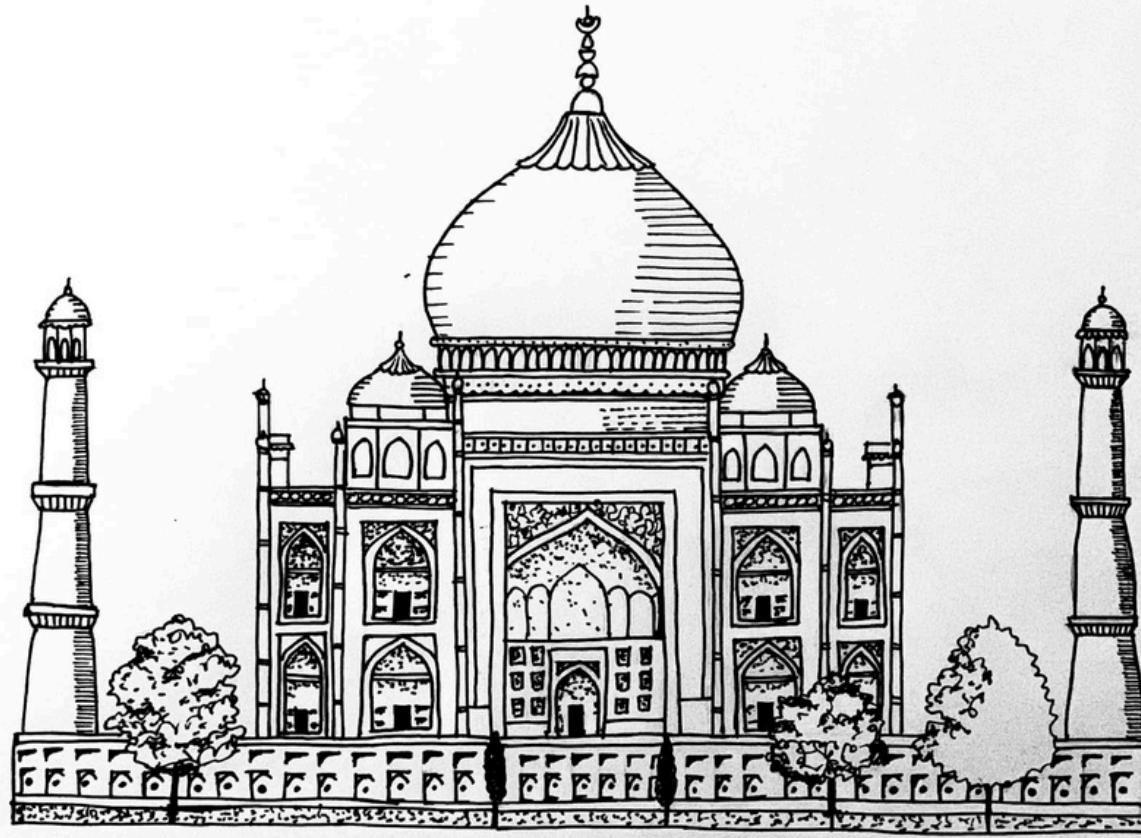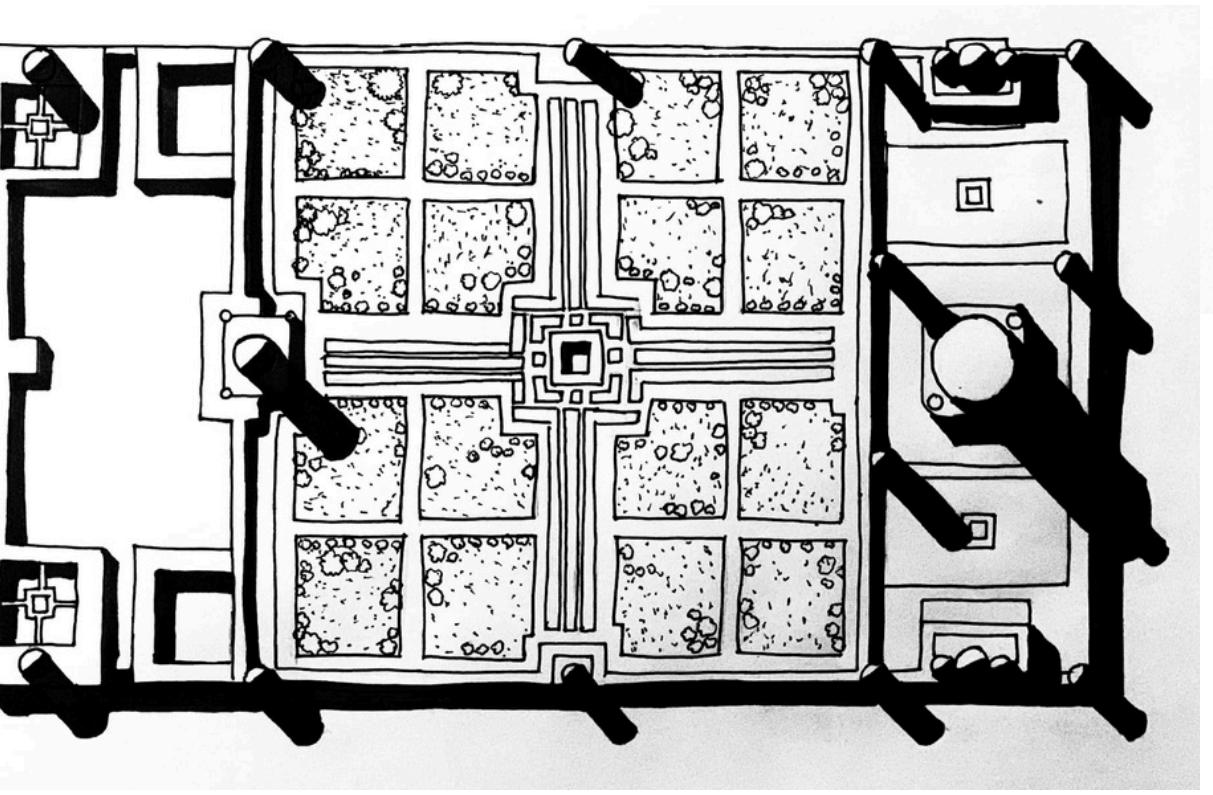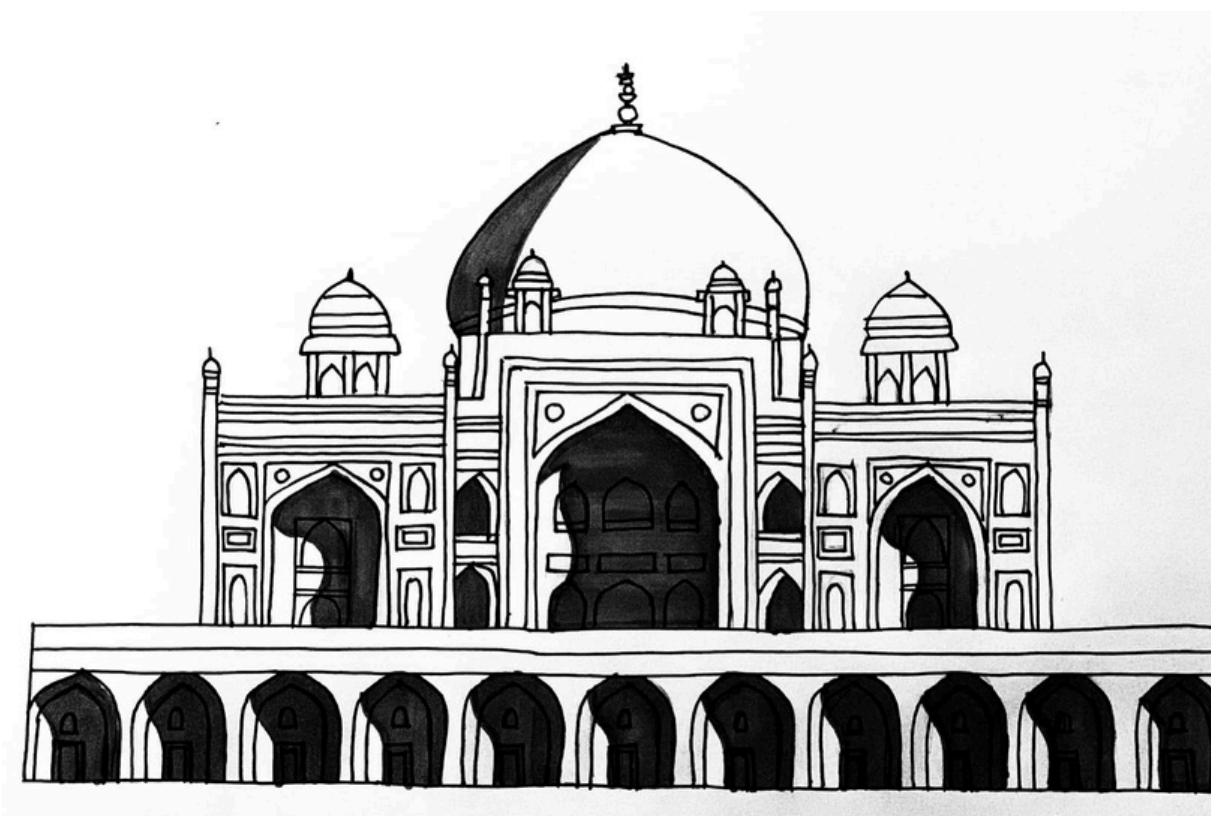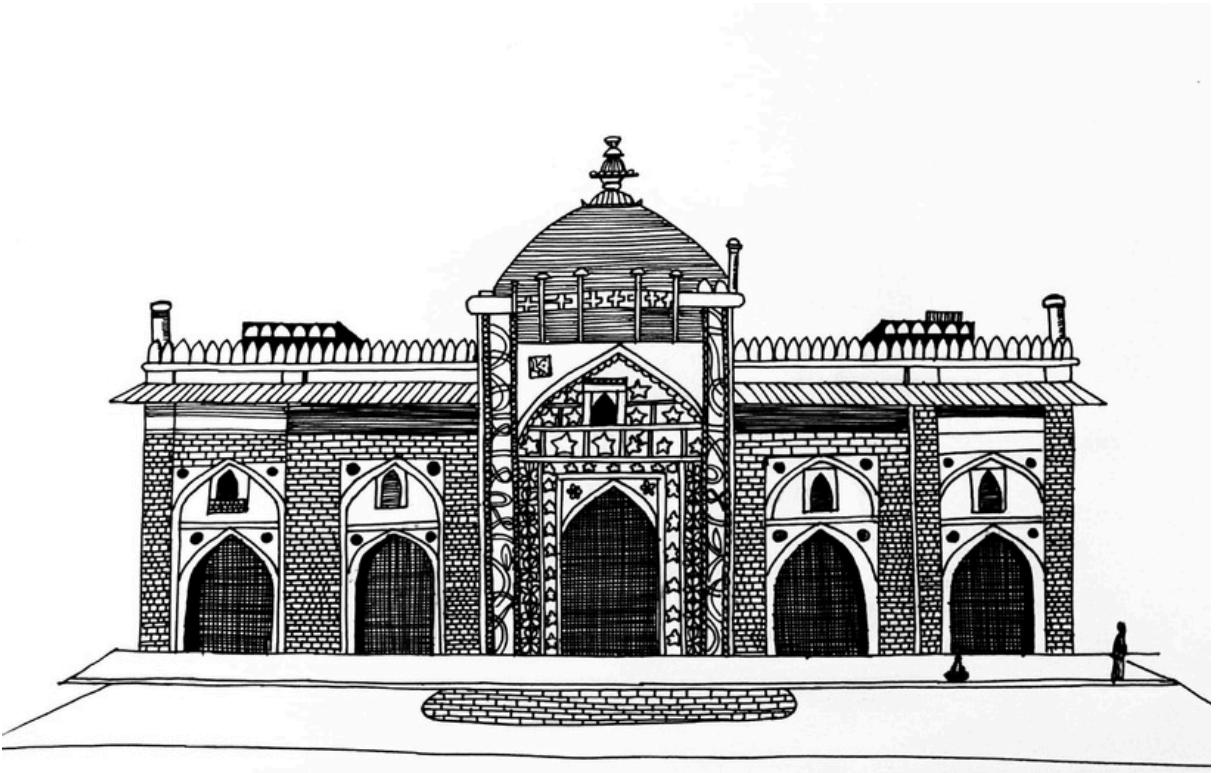

# Photography

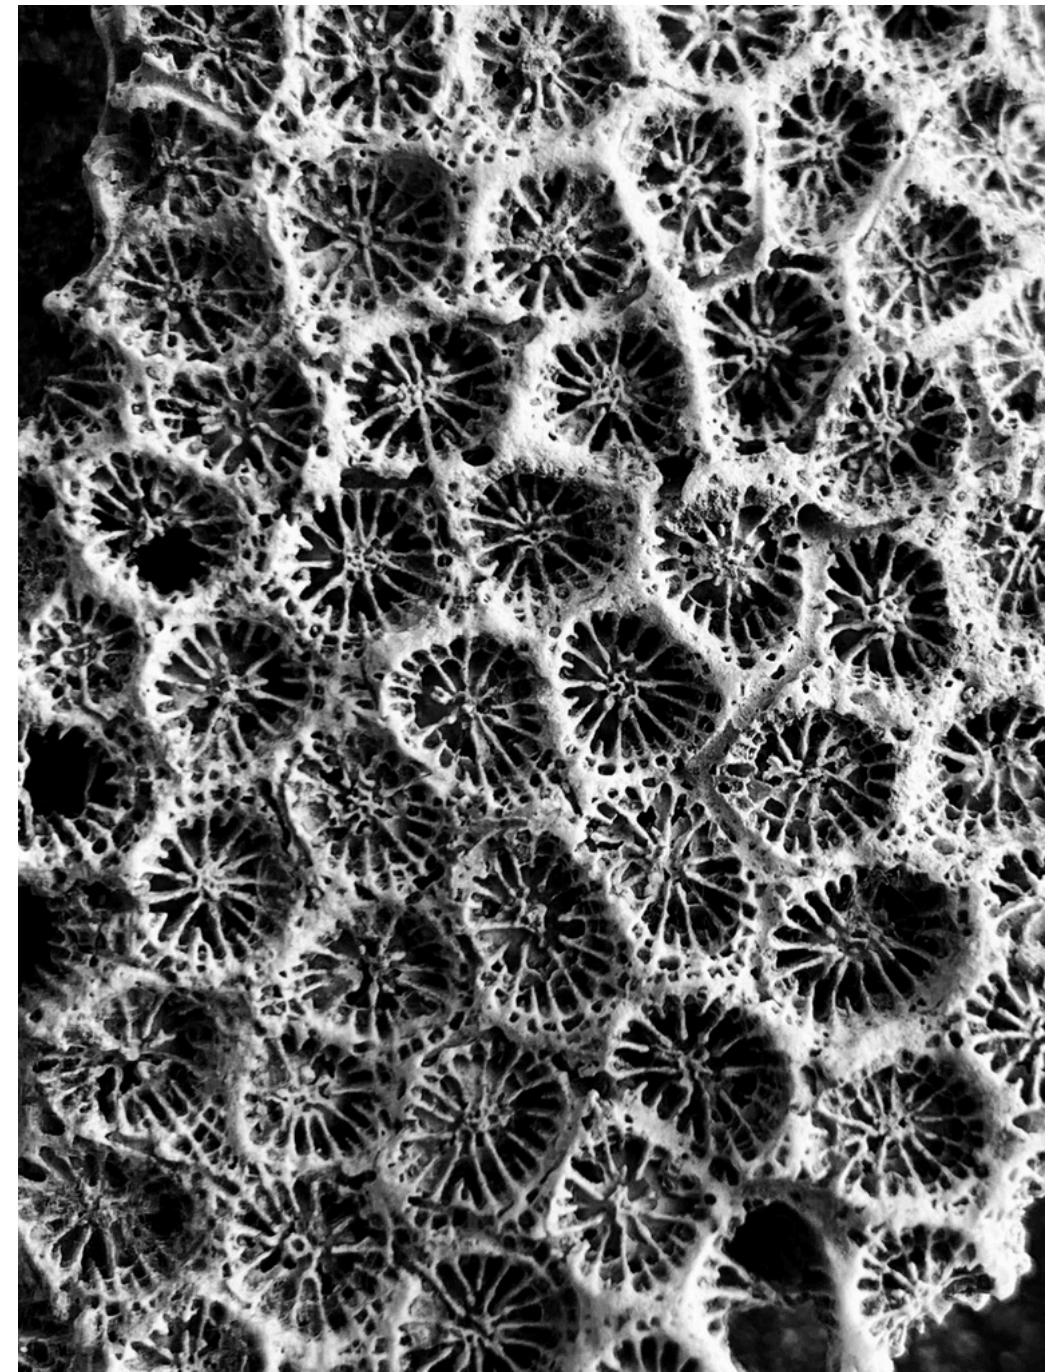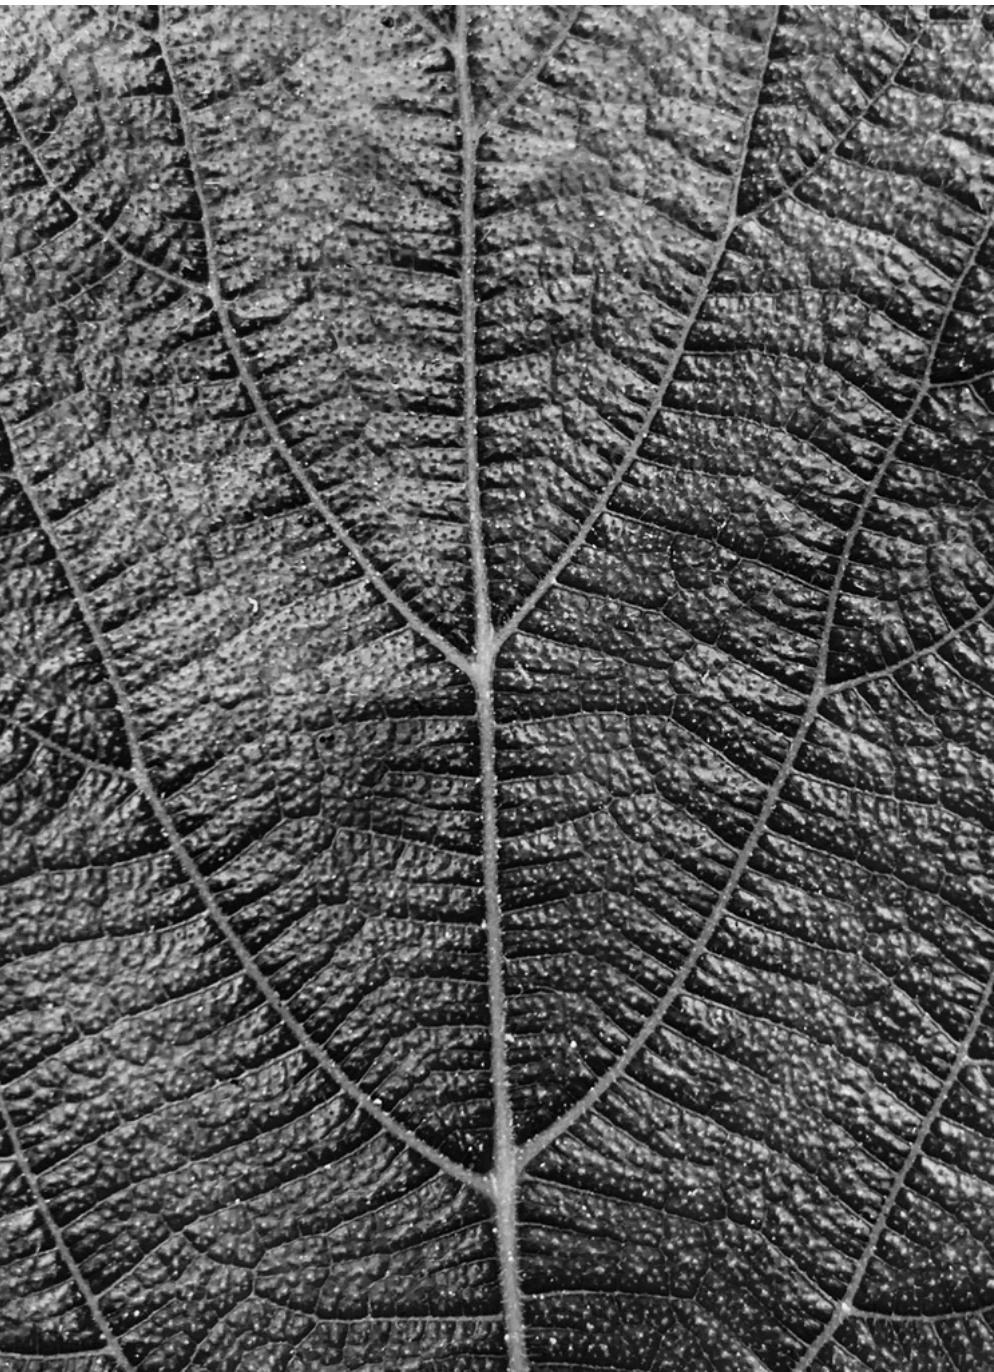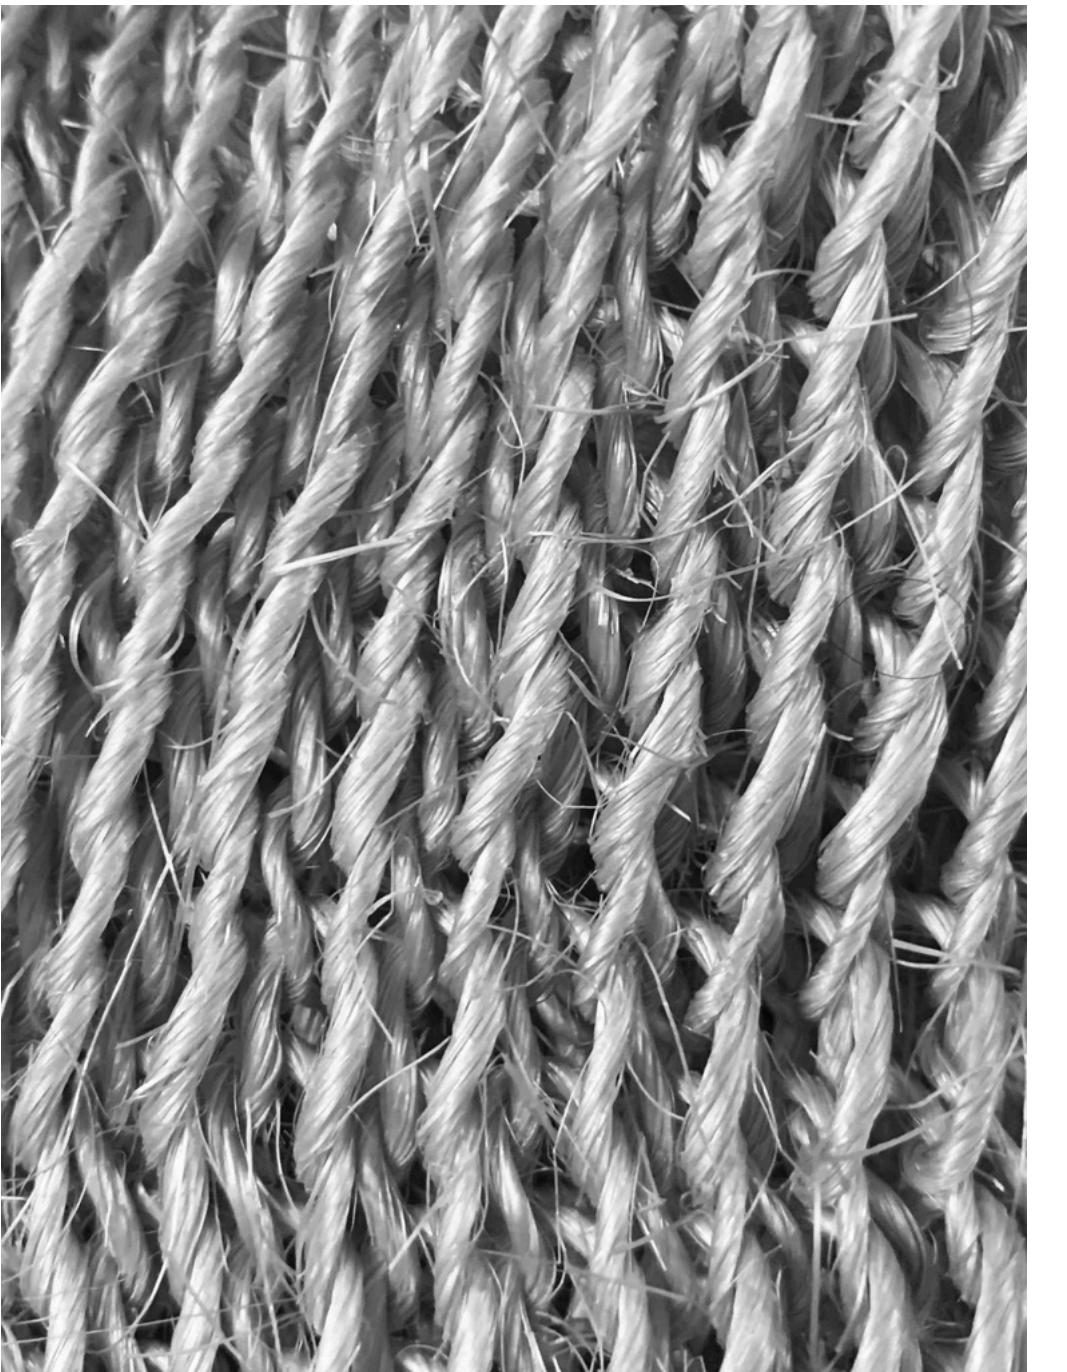

# Photography

